


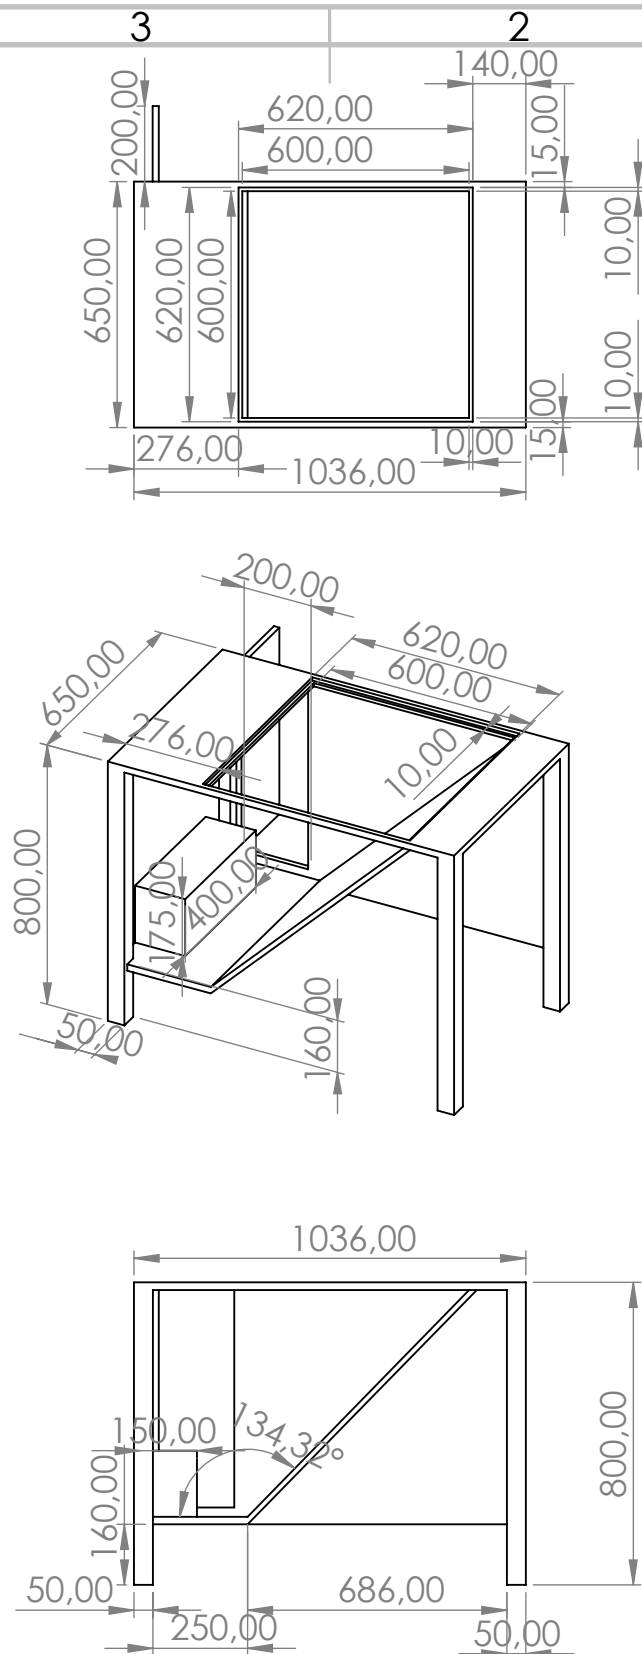

SAUF INDICATION CONTRAIRE: LES COTES SONT EN MILLIMETRES ETAT DE SURFACE: TOLERANCES: LINEAIRES: ANGULAIRES:						FINITION:		CASSER LES ANGES VIFS		NE PAS CHANGER L'ECHELLE		REVISION					
	NOM	SIGNATURE		DATE				TITRE:									
AUTEUR																	
VERIF.																	
APPR.																	
FAB.																	
QUAL.								MATERIAU:				No. DE PLAN					
								Final-TableV3 60x60_marge_8								A4	
								MASSE:				ECHELLE:1:20				FEUILLE 1 SUR 1	